




Frente

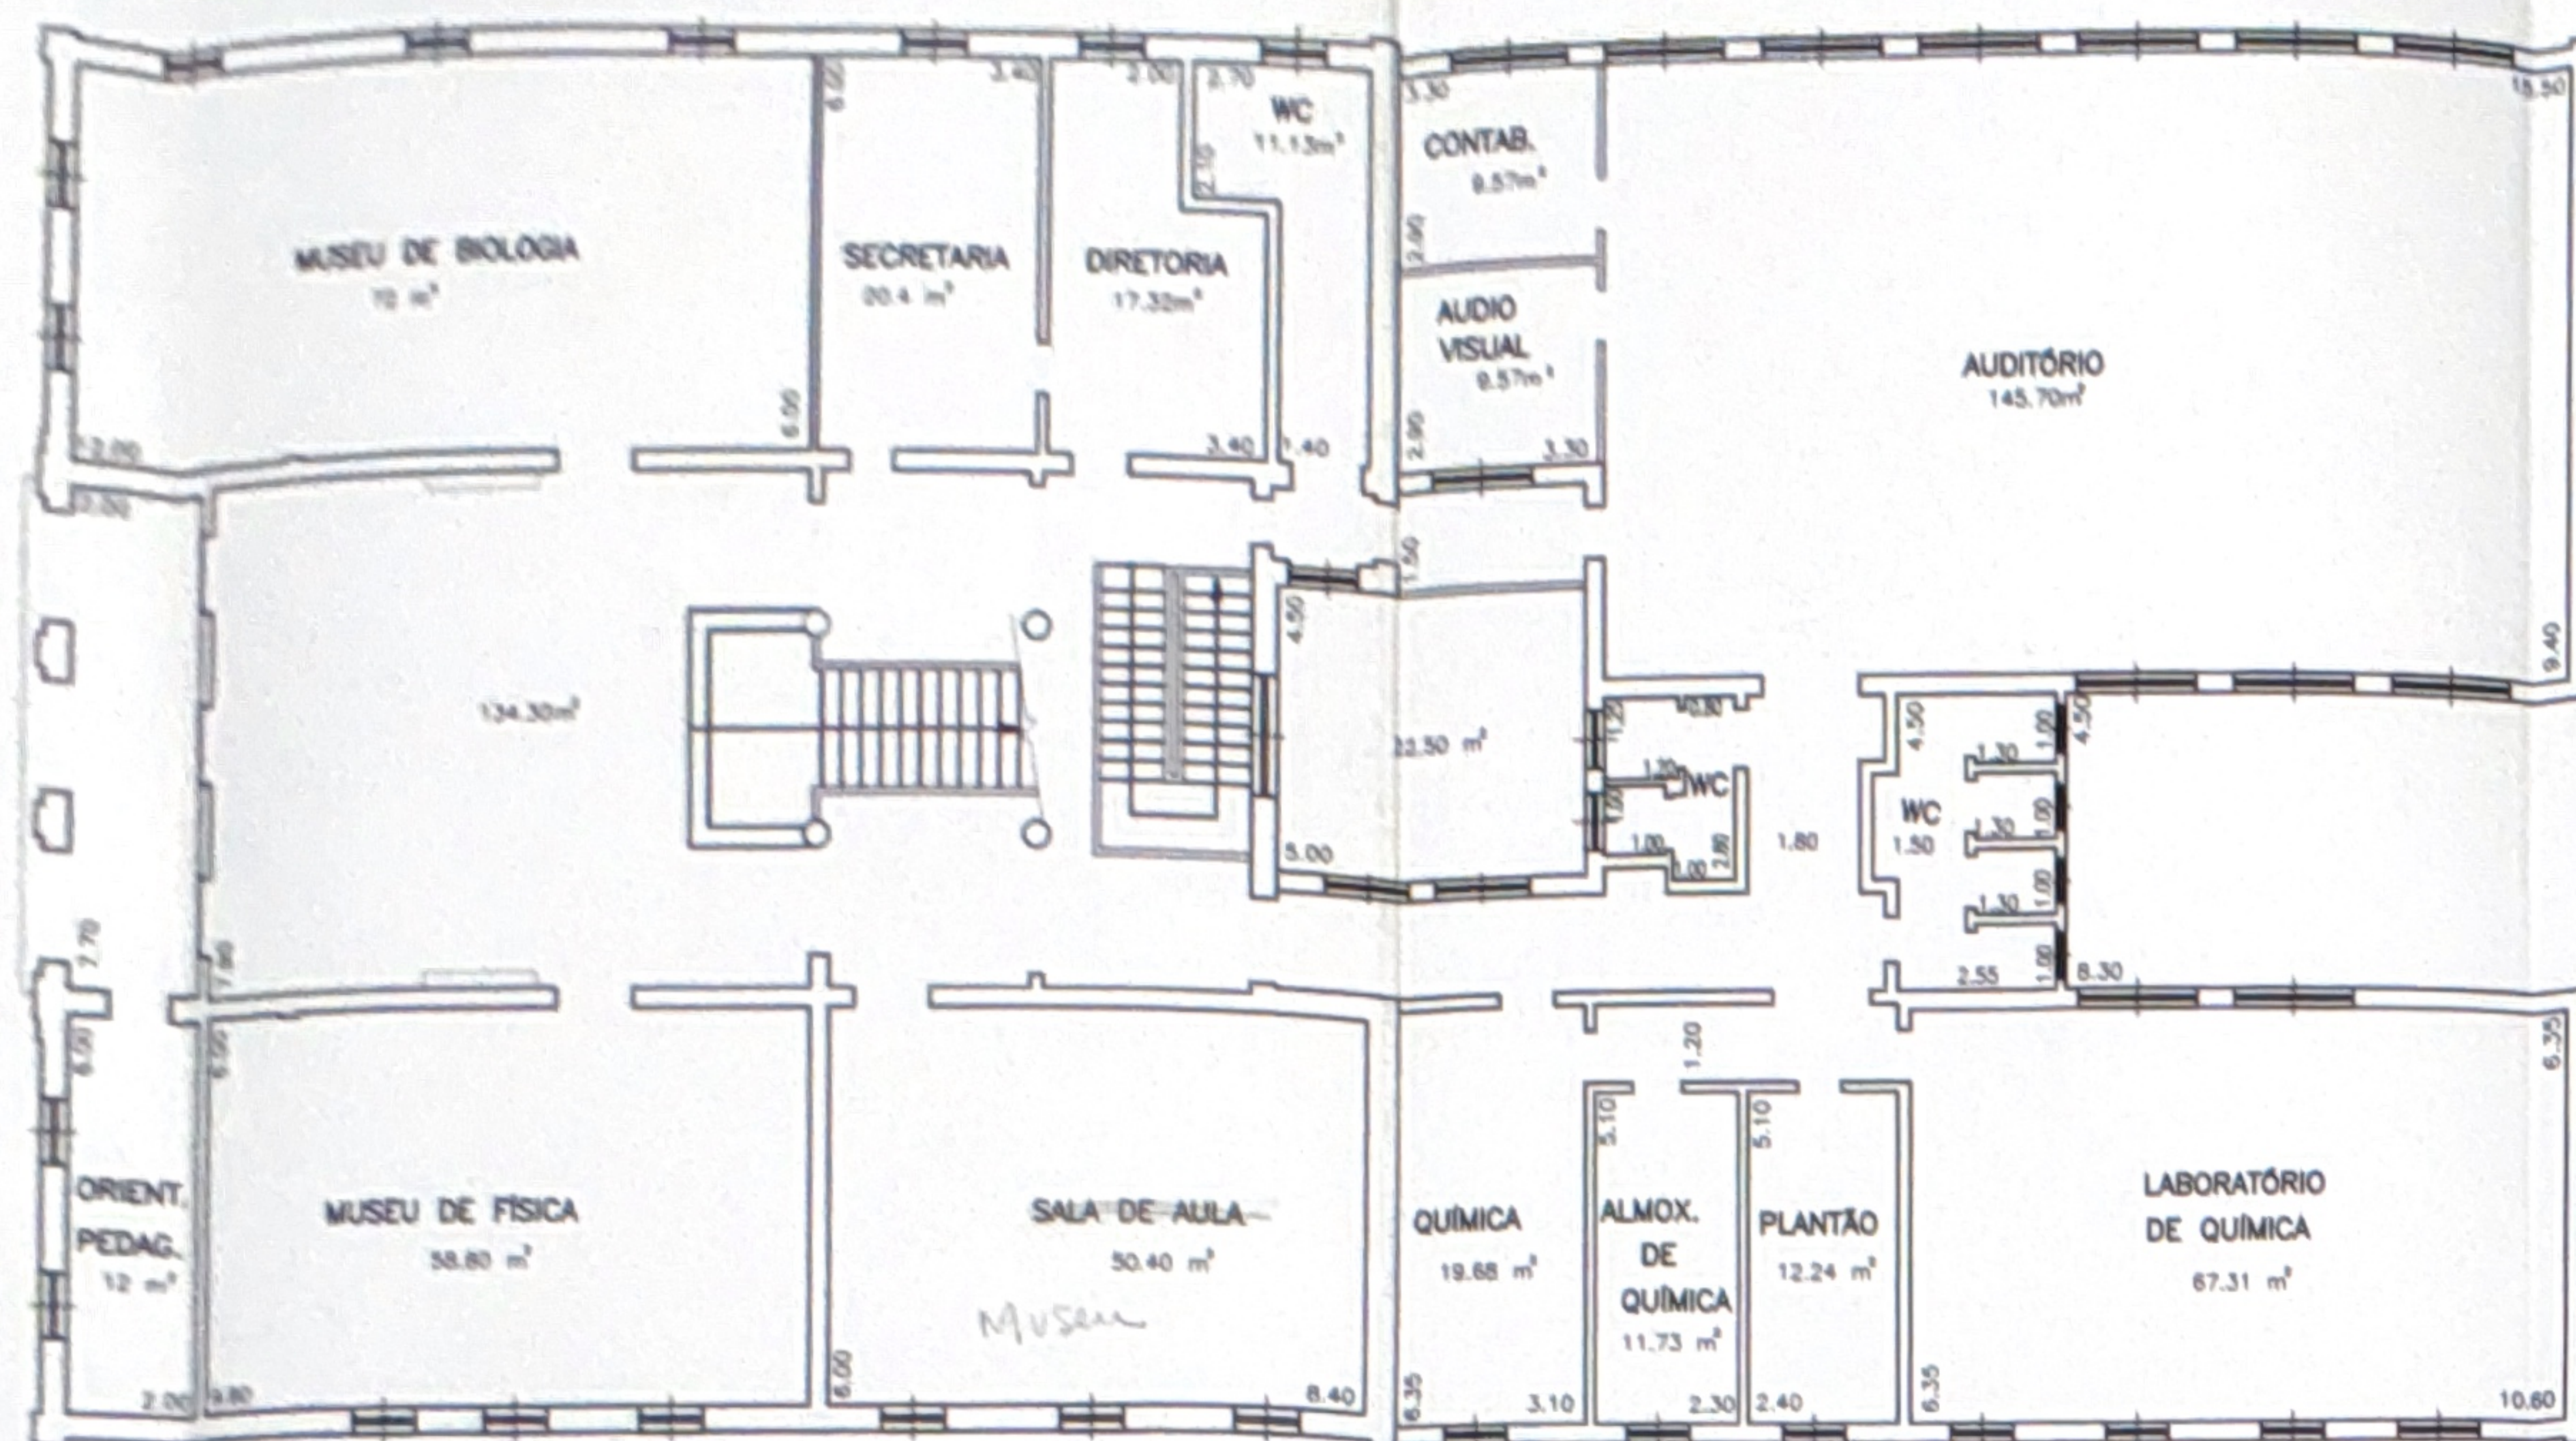

PLANTA DO TERREO-ESCALA 1:100

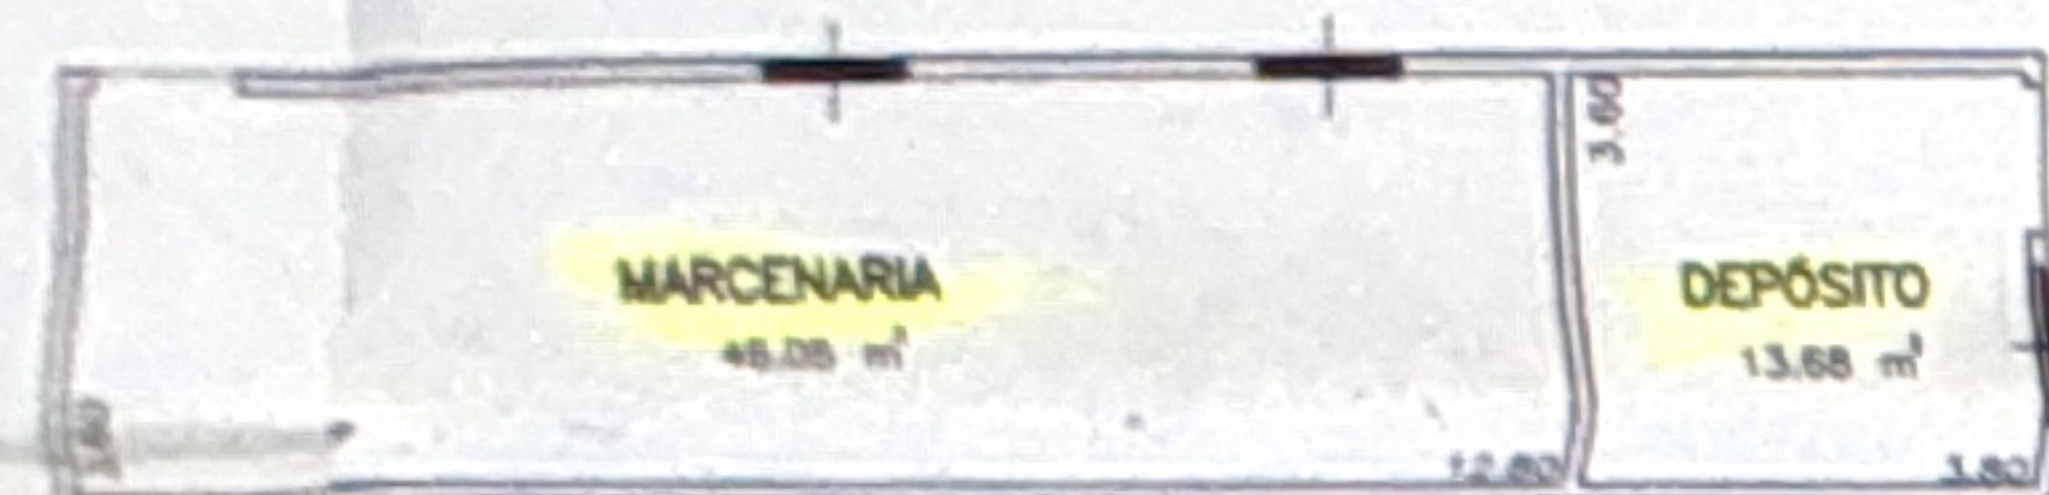


Frente

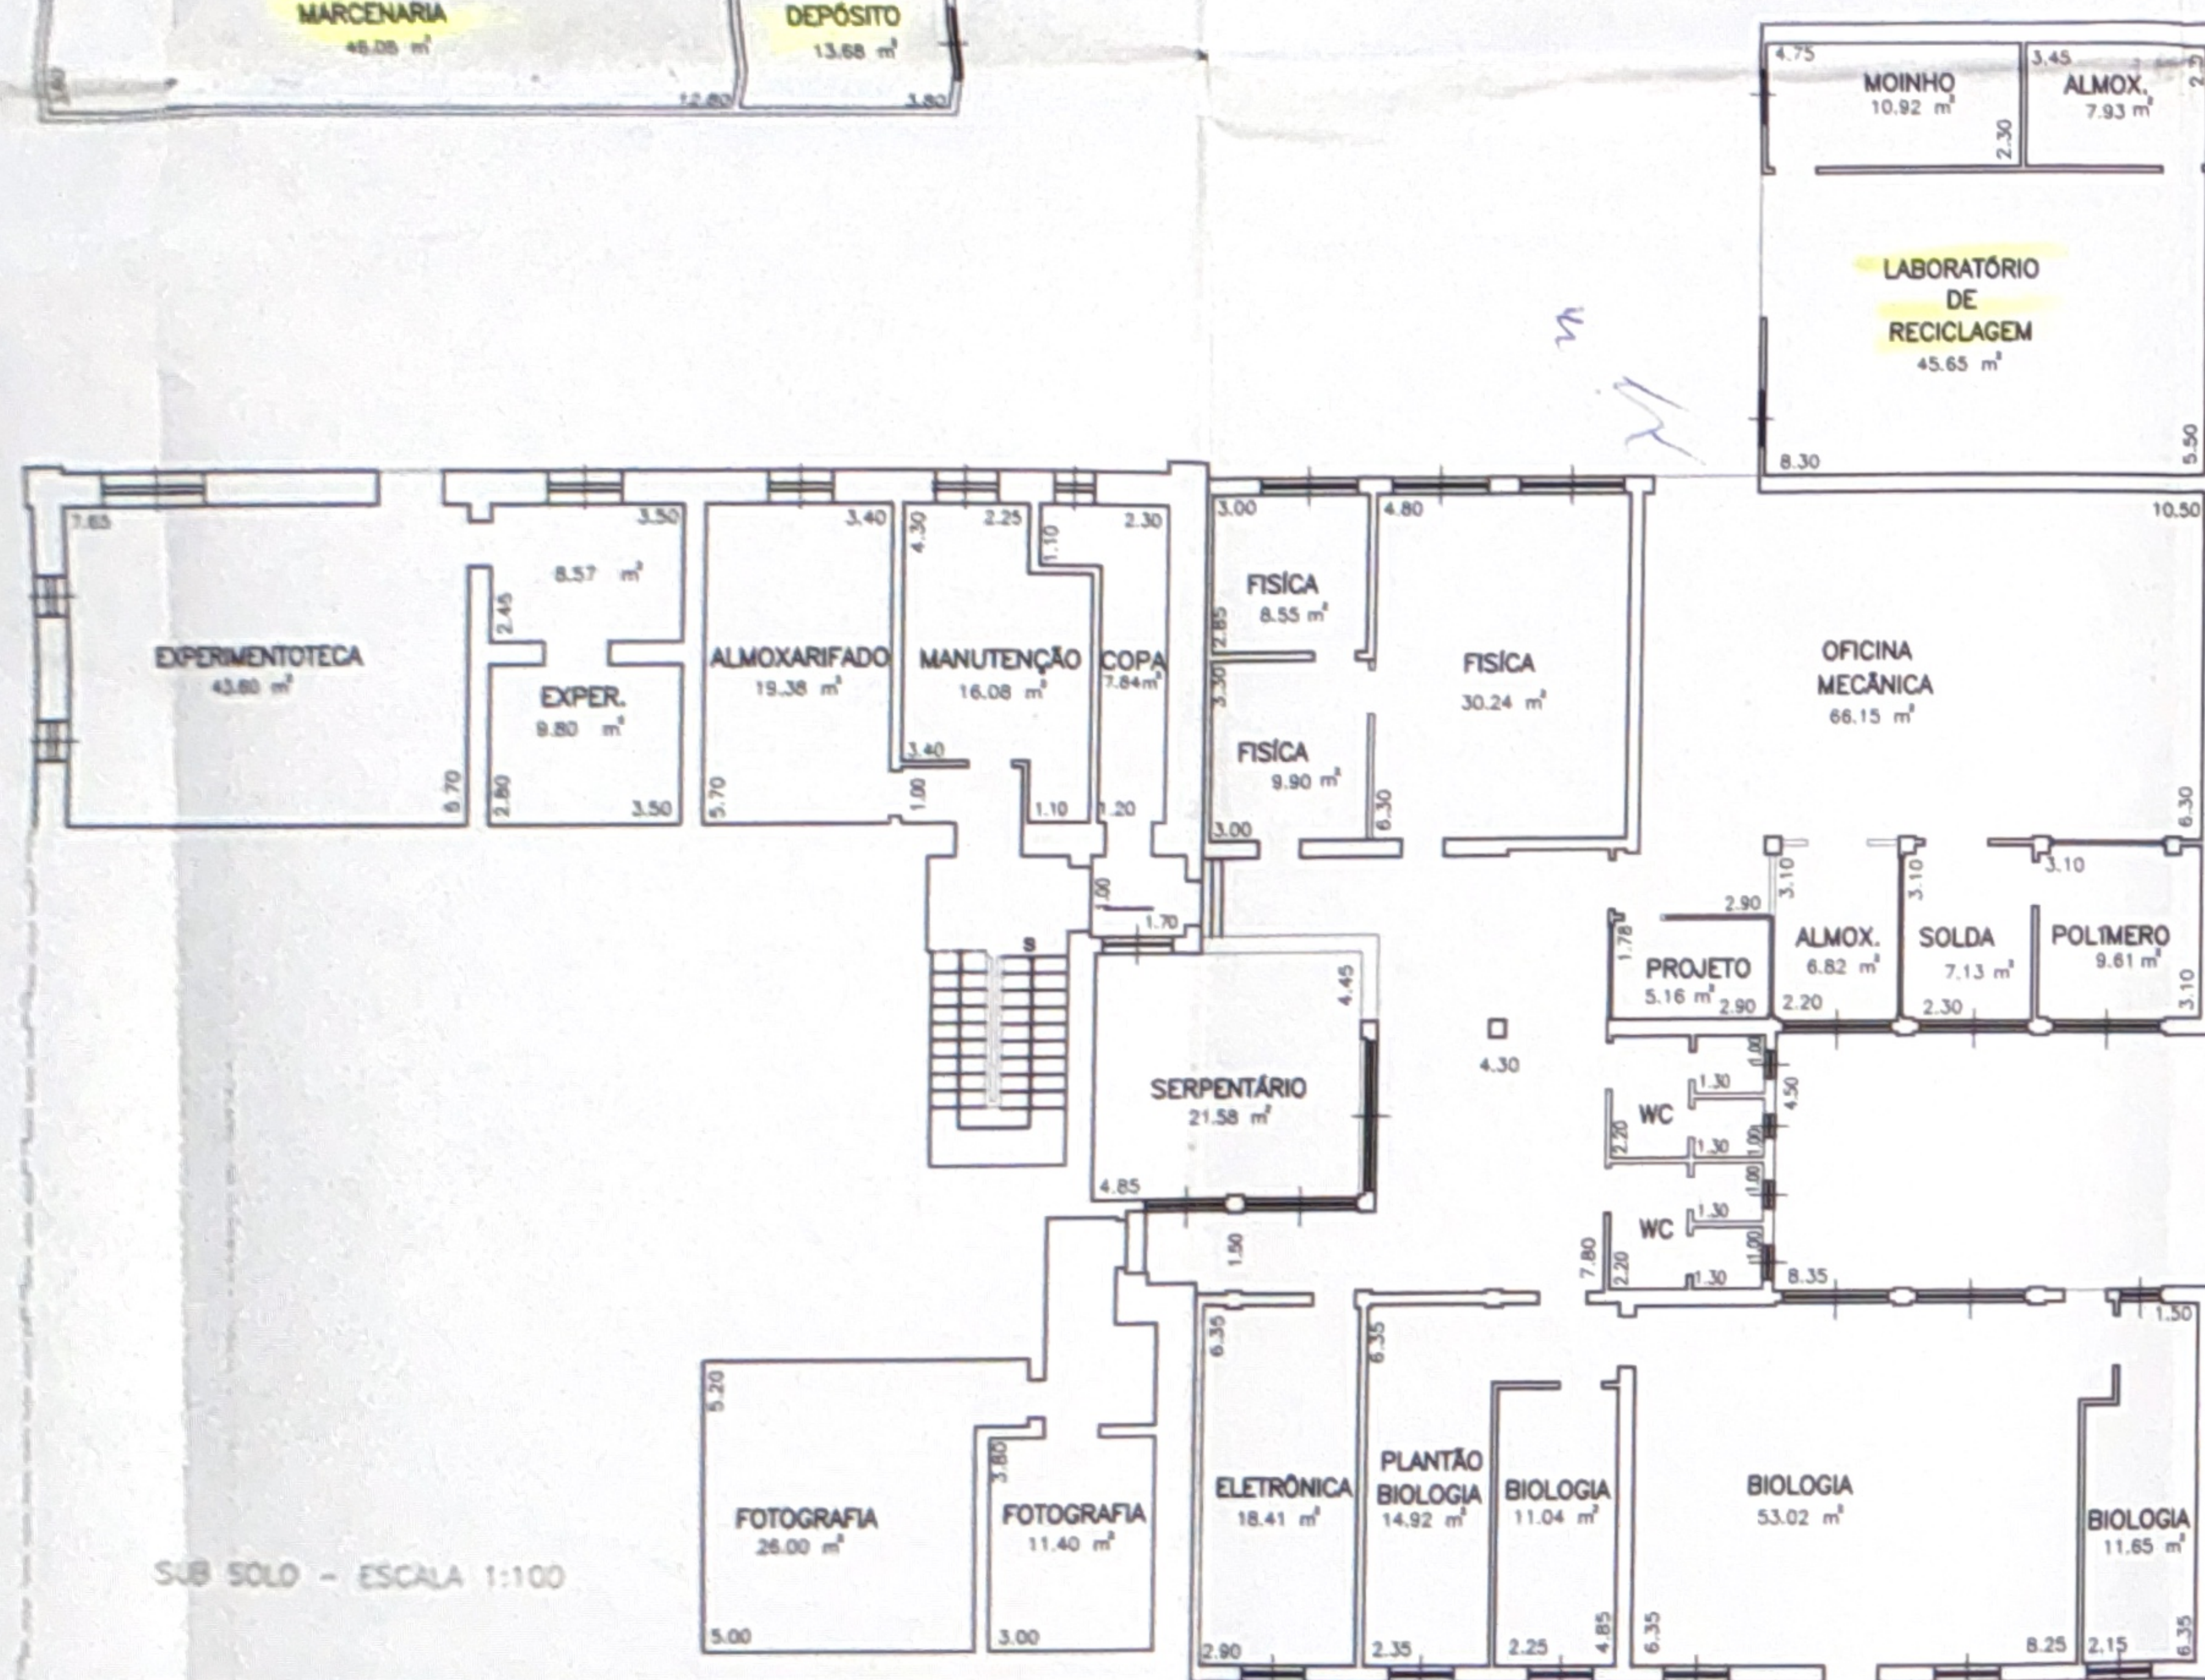

SUB SOLO - ESCALA 1:100

Frente

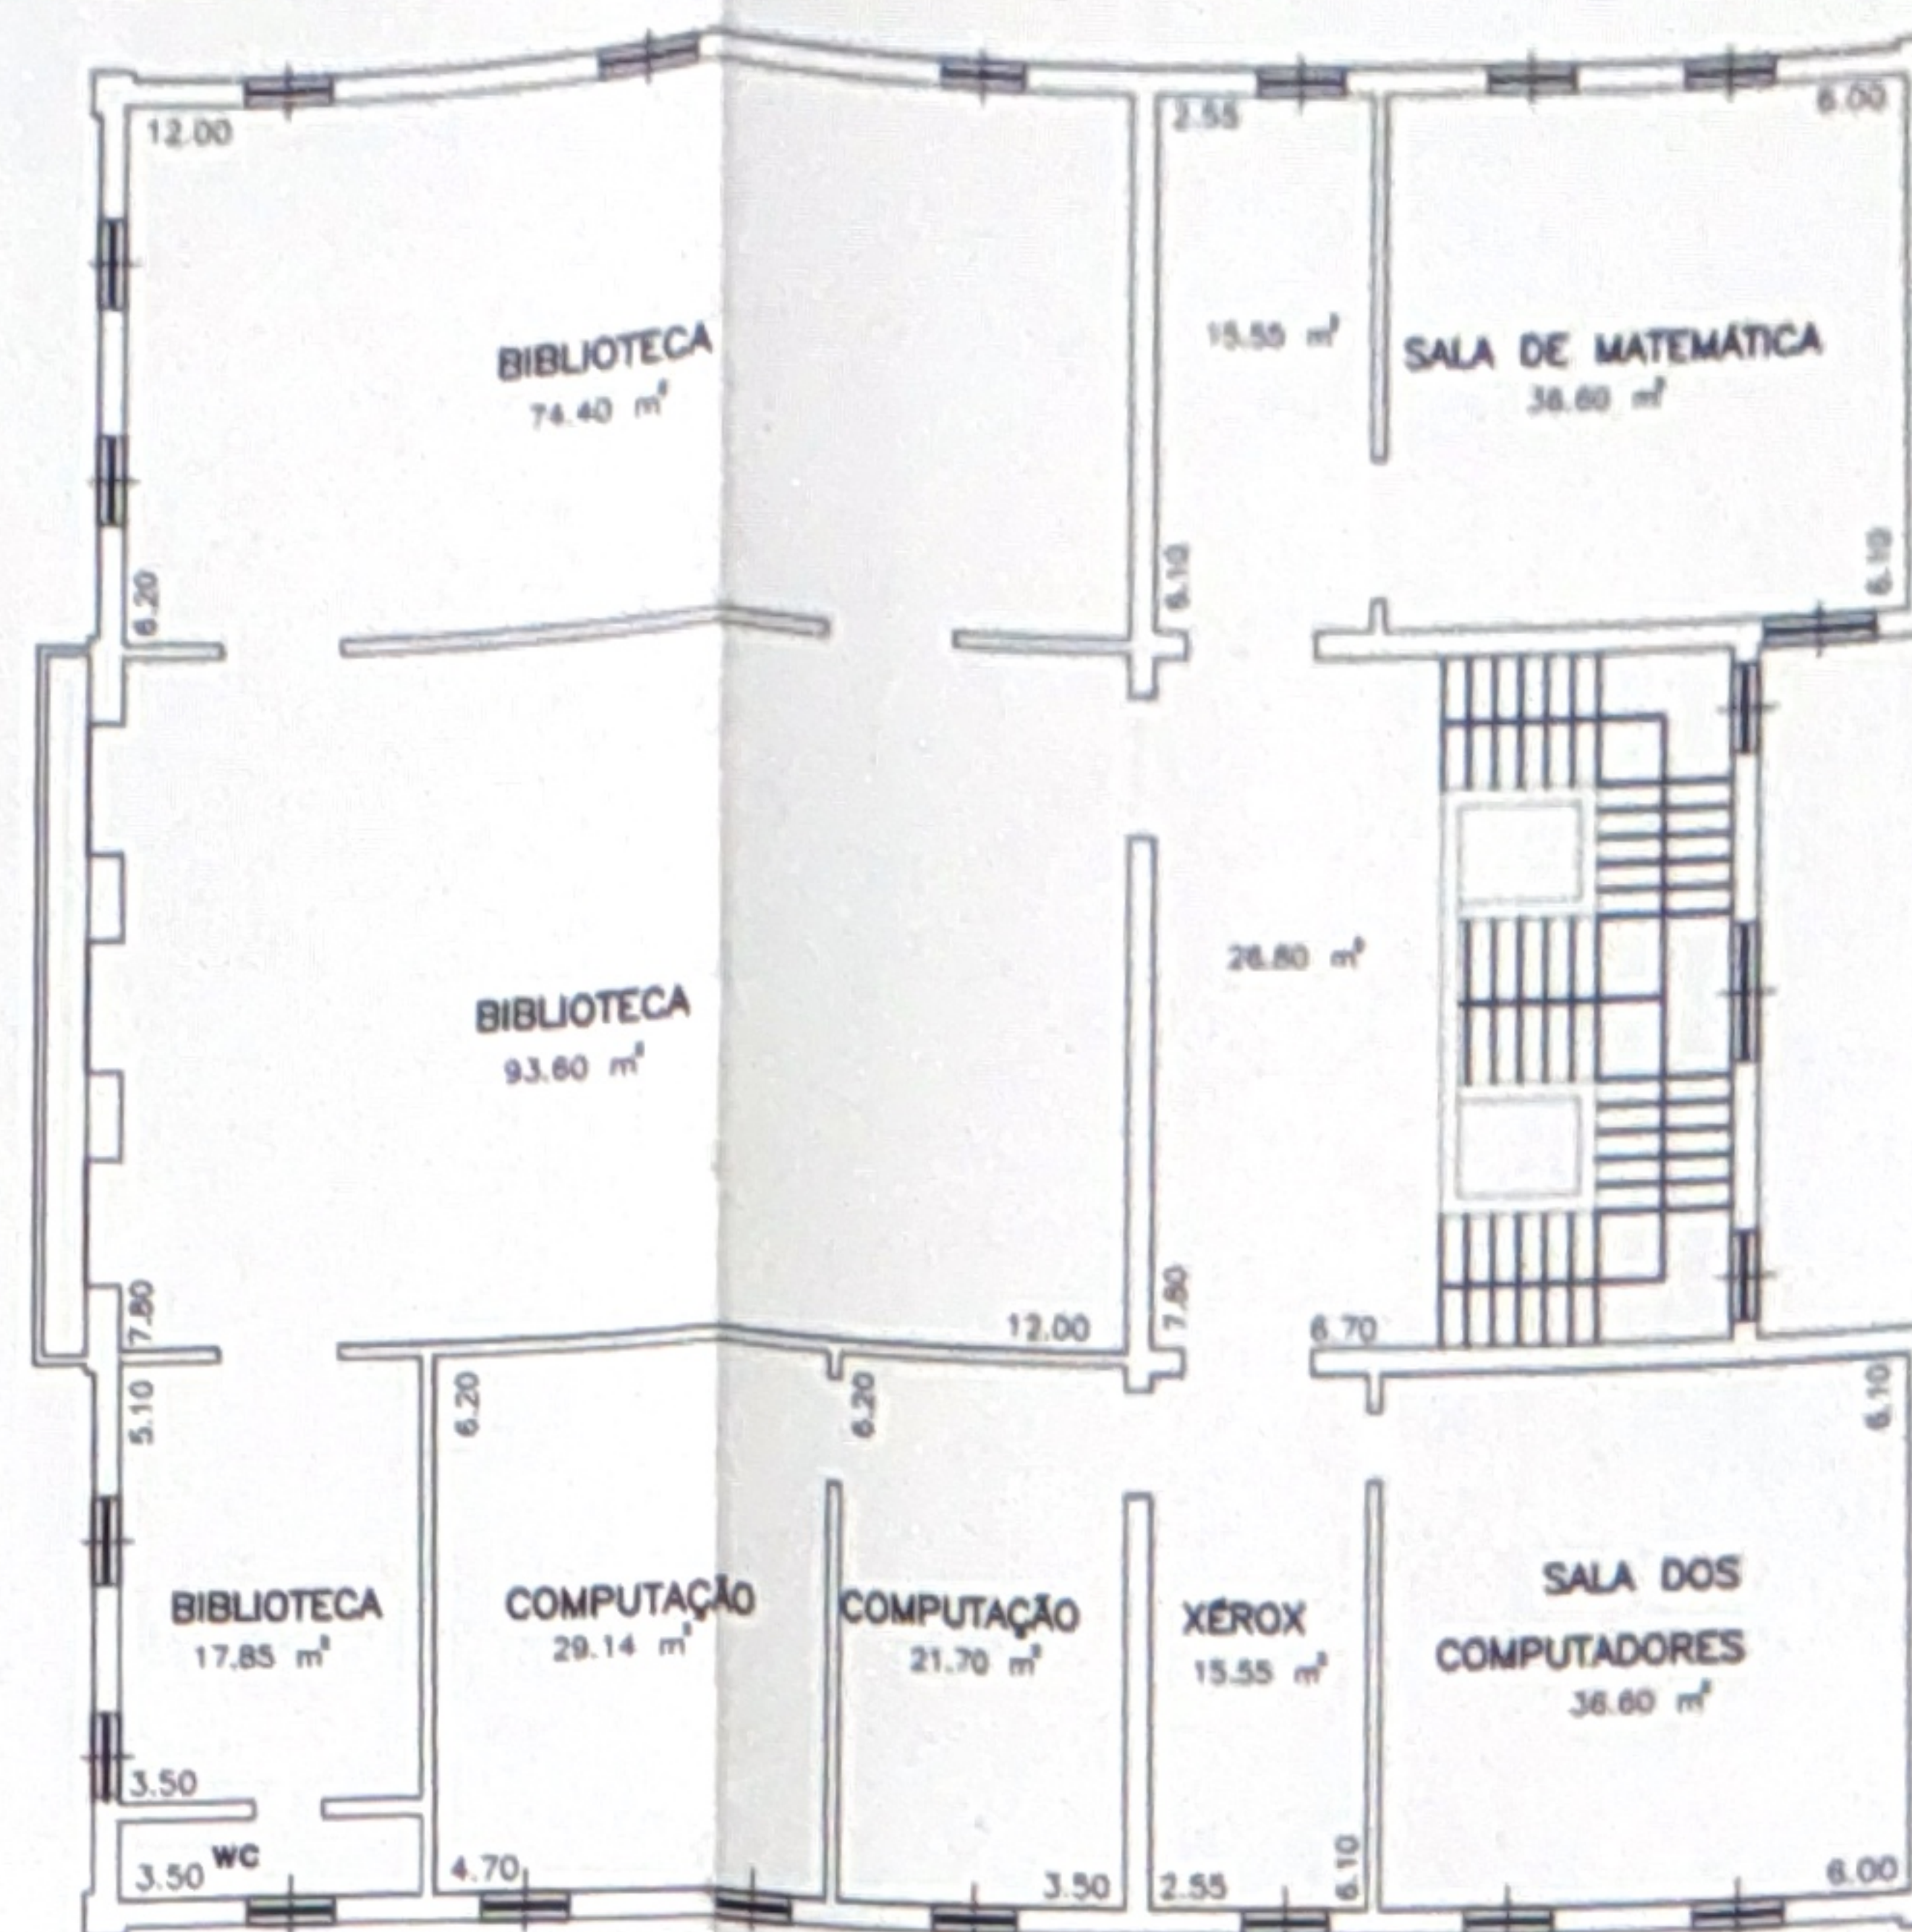

PRIMEIRO PAVIMENTO - ESCALA 1:100

PROJETO COMPLETO

FOLHA
ÚNICA

FINS : REGULARIZAÇÃO DE UM EDIFÍCIO

LOCAL: RUA NOVE DE JULHO 1227

BAIRRO: CENTRO

PROPRIETÁRIO: UNIVERSIDADE DE SÃO PAULO

ESCALAS: INDICADA

UNIDADE: METRO

SITUAÇÃO S/ ESCALA



DECLARO QUE A APROVAÇÃO DO PROJETO NÃO IMPLICA NO RECONHECIMENTO POR PARTE DA PREFEITURA DO DIGNO DE PROPRIEDADE DO TERRENO

Pharmaceuticals

ALTO DO PROJETO E RESP. TÉCNICO
ENG. CIVIL :
CROB. :


10

ÁREAS m ²	
TERRENO	1.612.03 m ²
ÁREA LIVRE	570.88 m ²
SUB-SOLO	631.56 m ²
TERREO	855.06 m ²
PRIMEIRO PAVIMENTO	450.00 m ²
TOTAL	1.936.62 m ²



Sidhu @ Edcc. 22/11/2018