



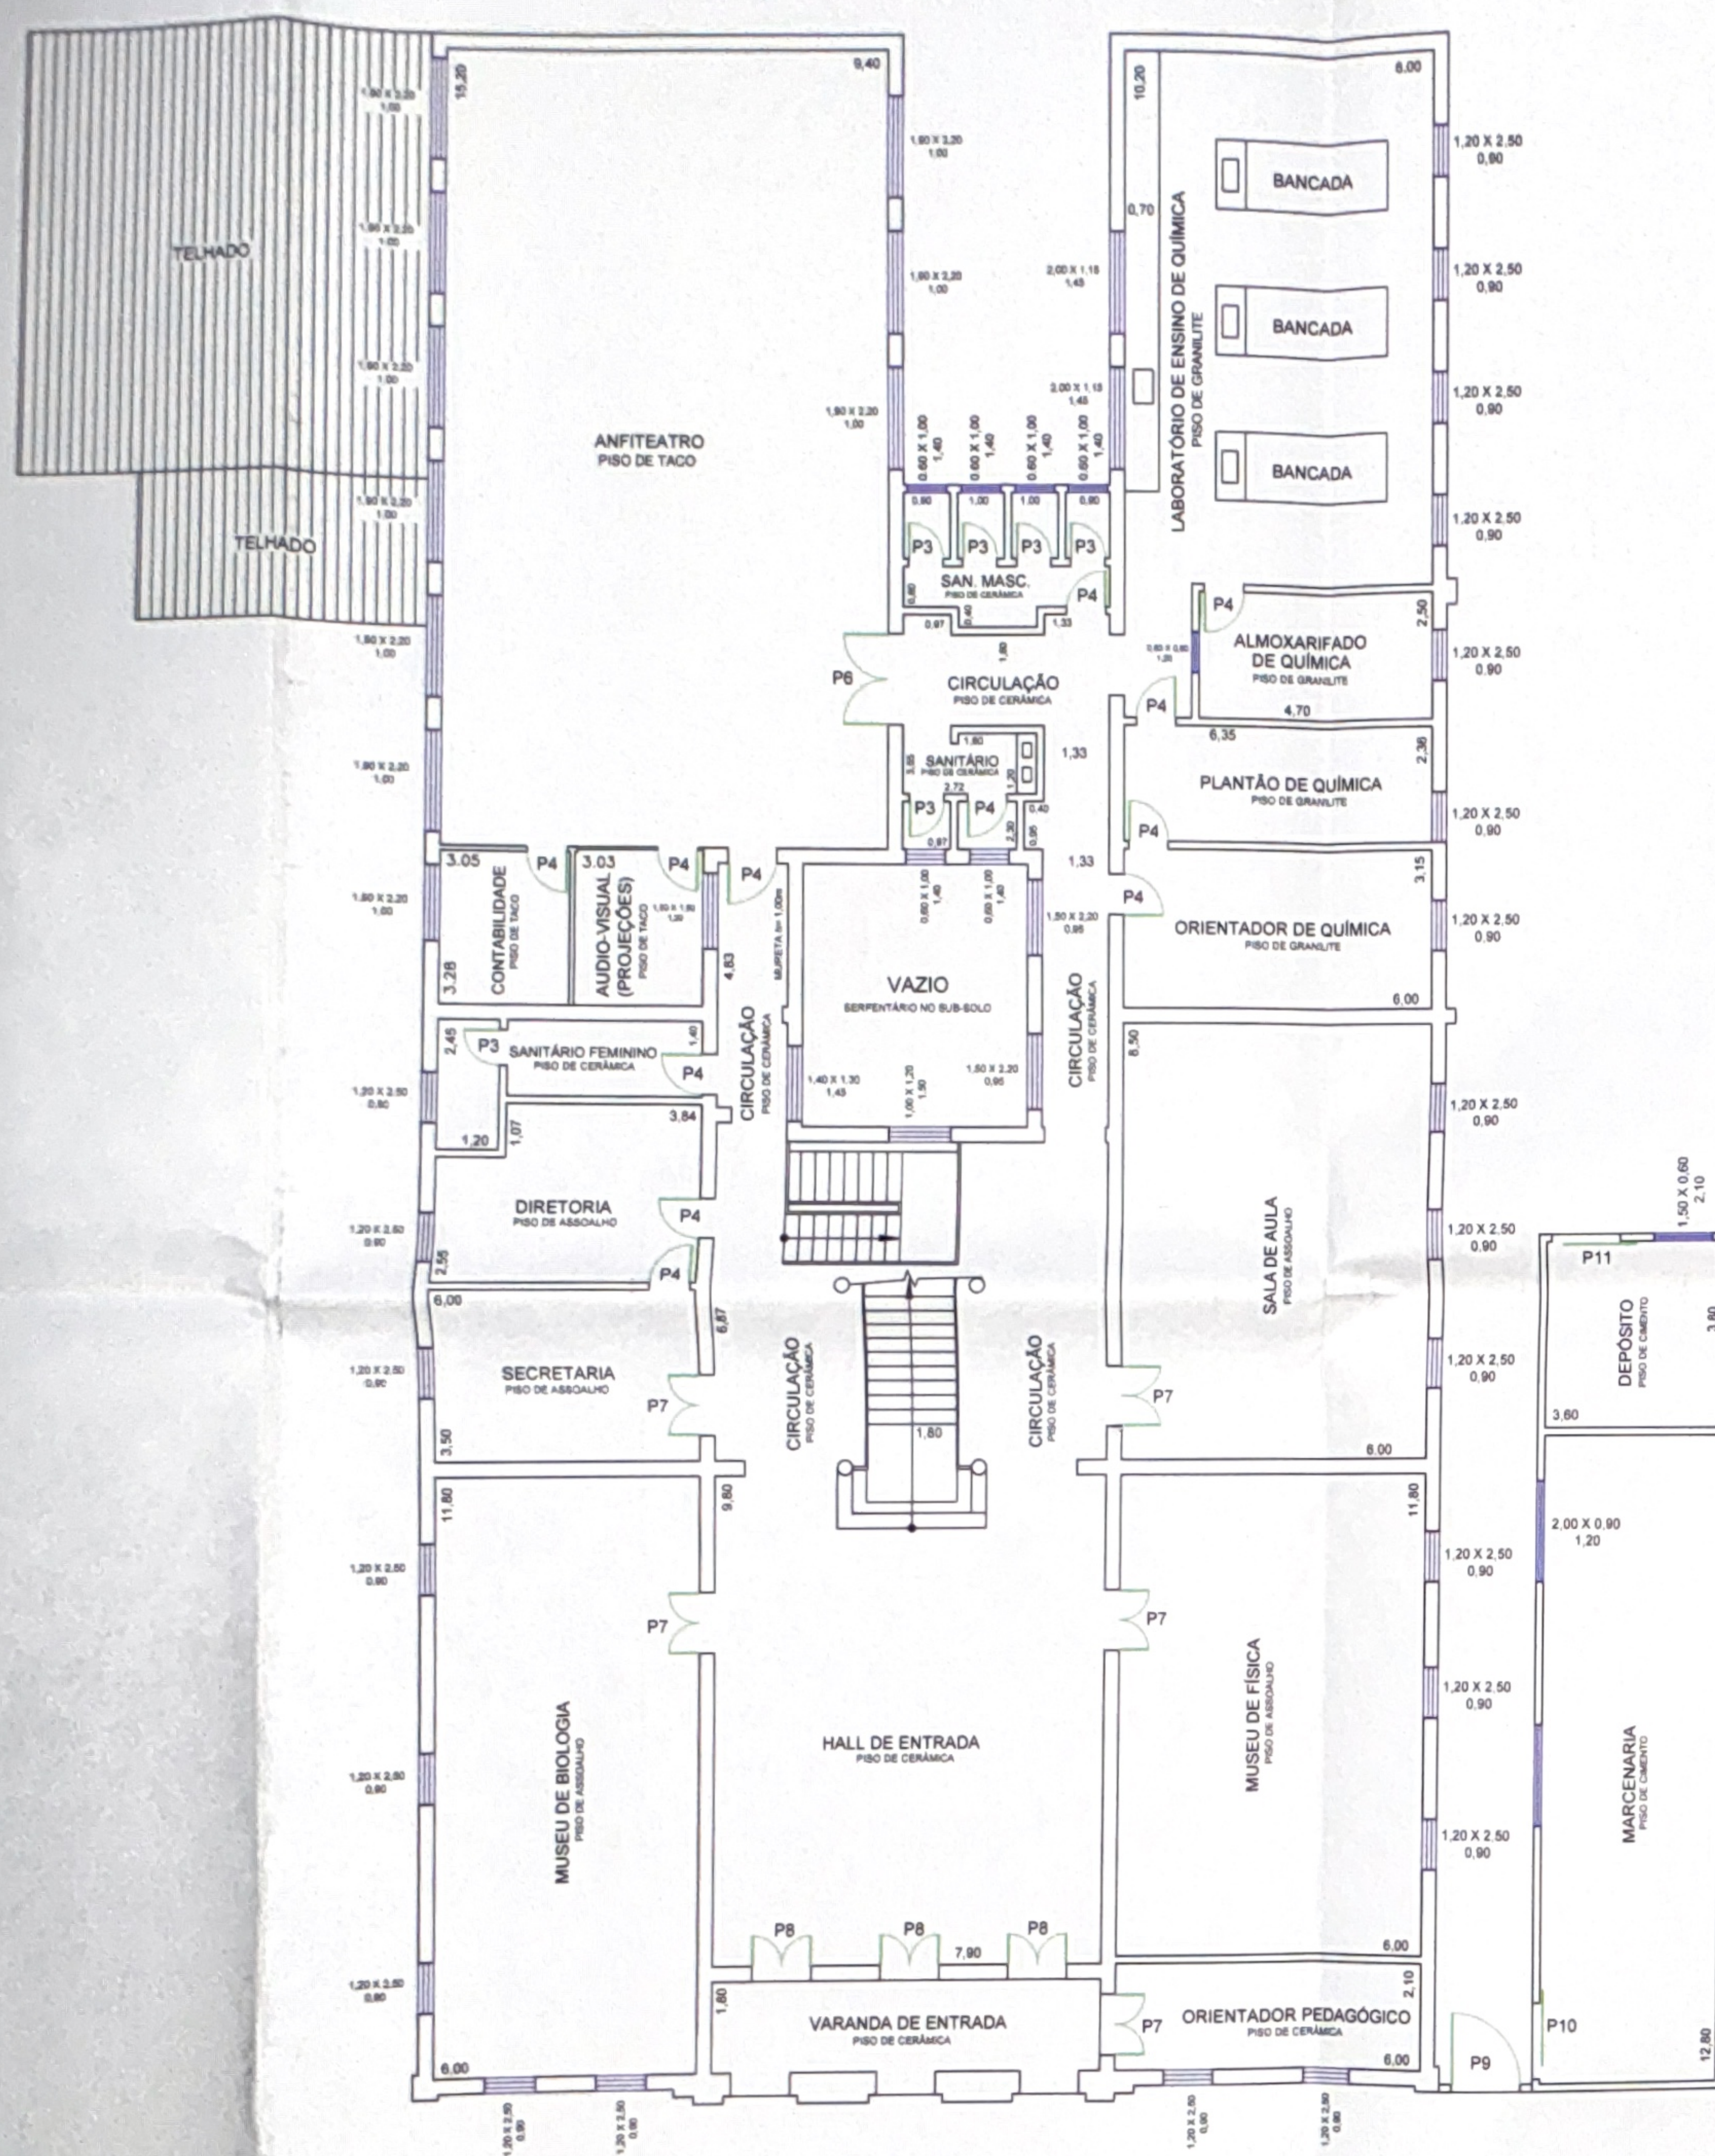

PAVIMENTO TÉRREO

TABELA DE PORTAS			
TIPO	DIMENSÃO	MATERIAL	QUANT.
P1	0,80 X 2,10	FERRO/VIDRO	05
P2	2,30 X 2,20	FERRO/VIDRO (CORRER)	02
P3	0,70 X 2,10	MADEIRA	10
P4	0,80 X 2,10	MADEIRA	27
P5	1,00 X 1,90	MADEIRA	01
P6	1,20 X 2,10	MADEIRA	01
P7	1,20 X 2,10	MADEIRA/VIDRO	12
P8	1,20 X 3,45	MADEIRA/VIDRO	03
P9	1,40 X 1,90	CHAPA DE FERRO	01
P10	1,50 X 2,10	FERRO/VIDRO (CORRER)	01
P11	1,40 X 1,90	FERRO/VIDRO (CORRER)	01
P12	1,50 X 3,00	MADEIRA/VIDRO	05
P13	1,70 X 2,85	MADEIRA/VIDRO	03

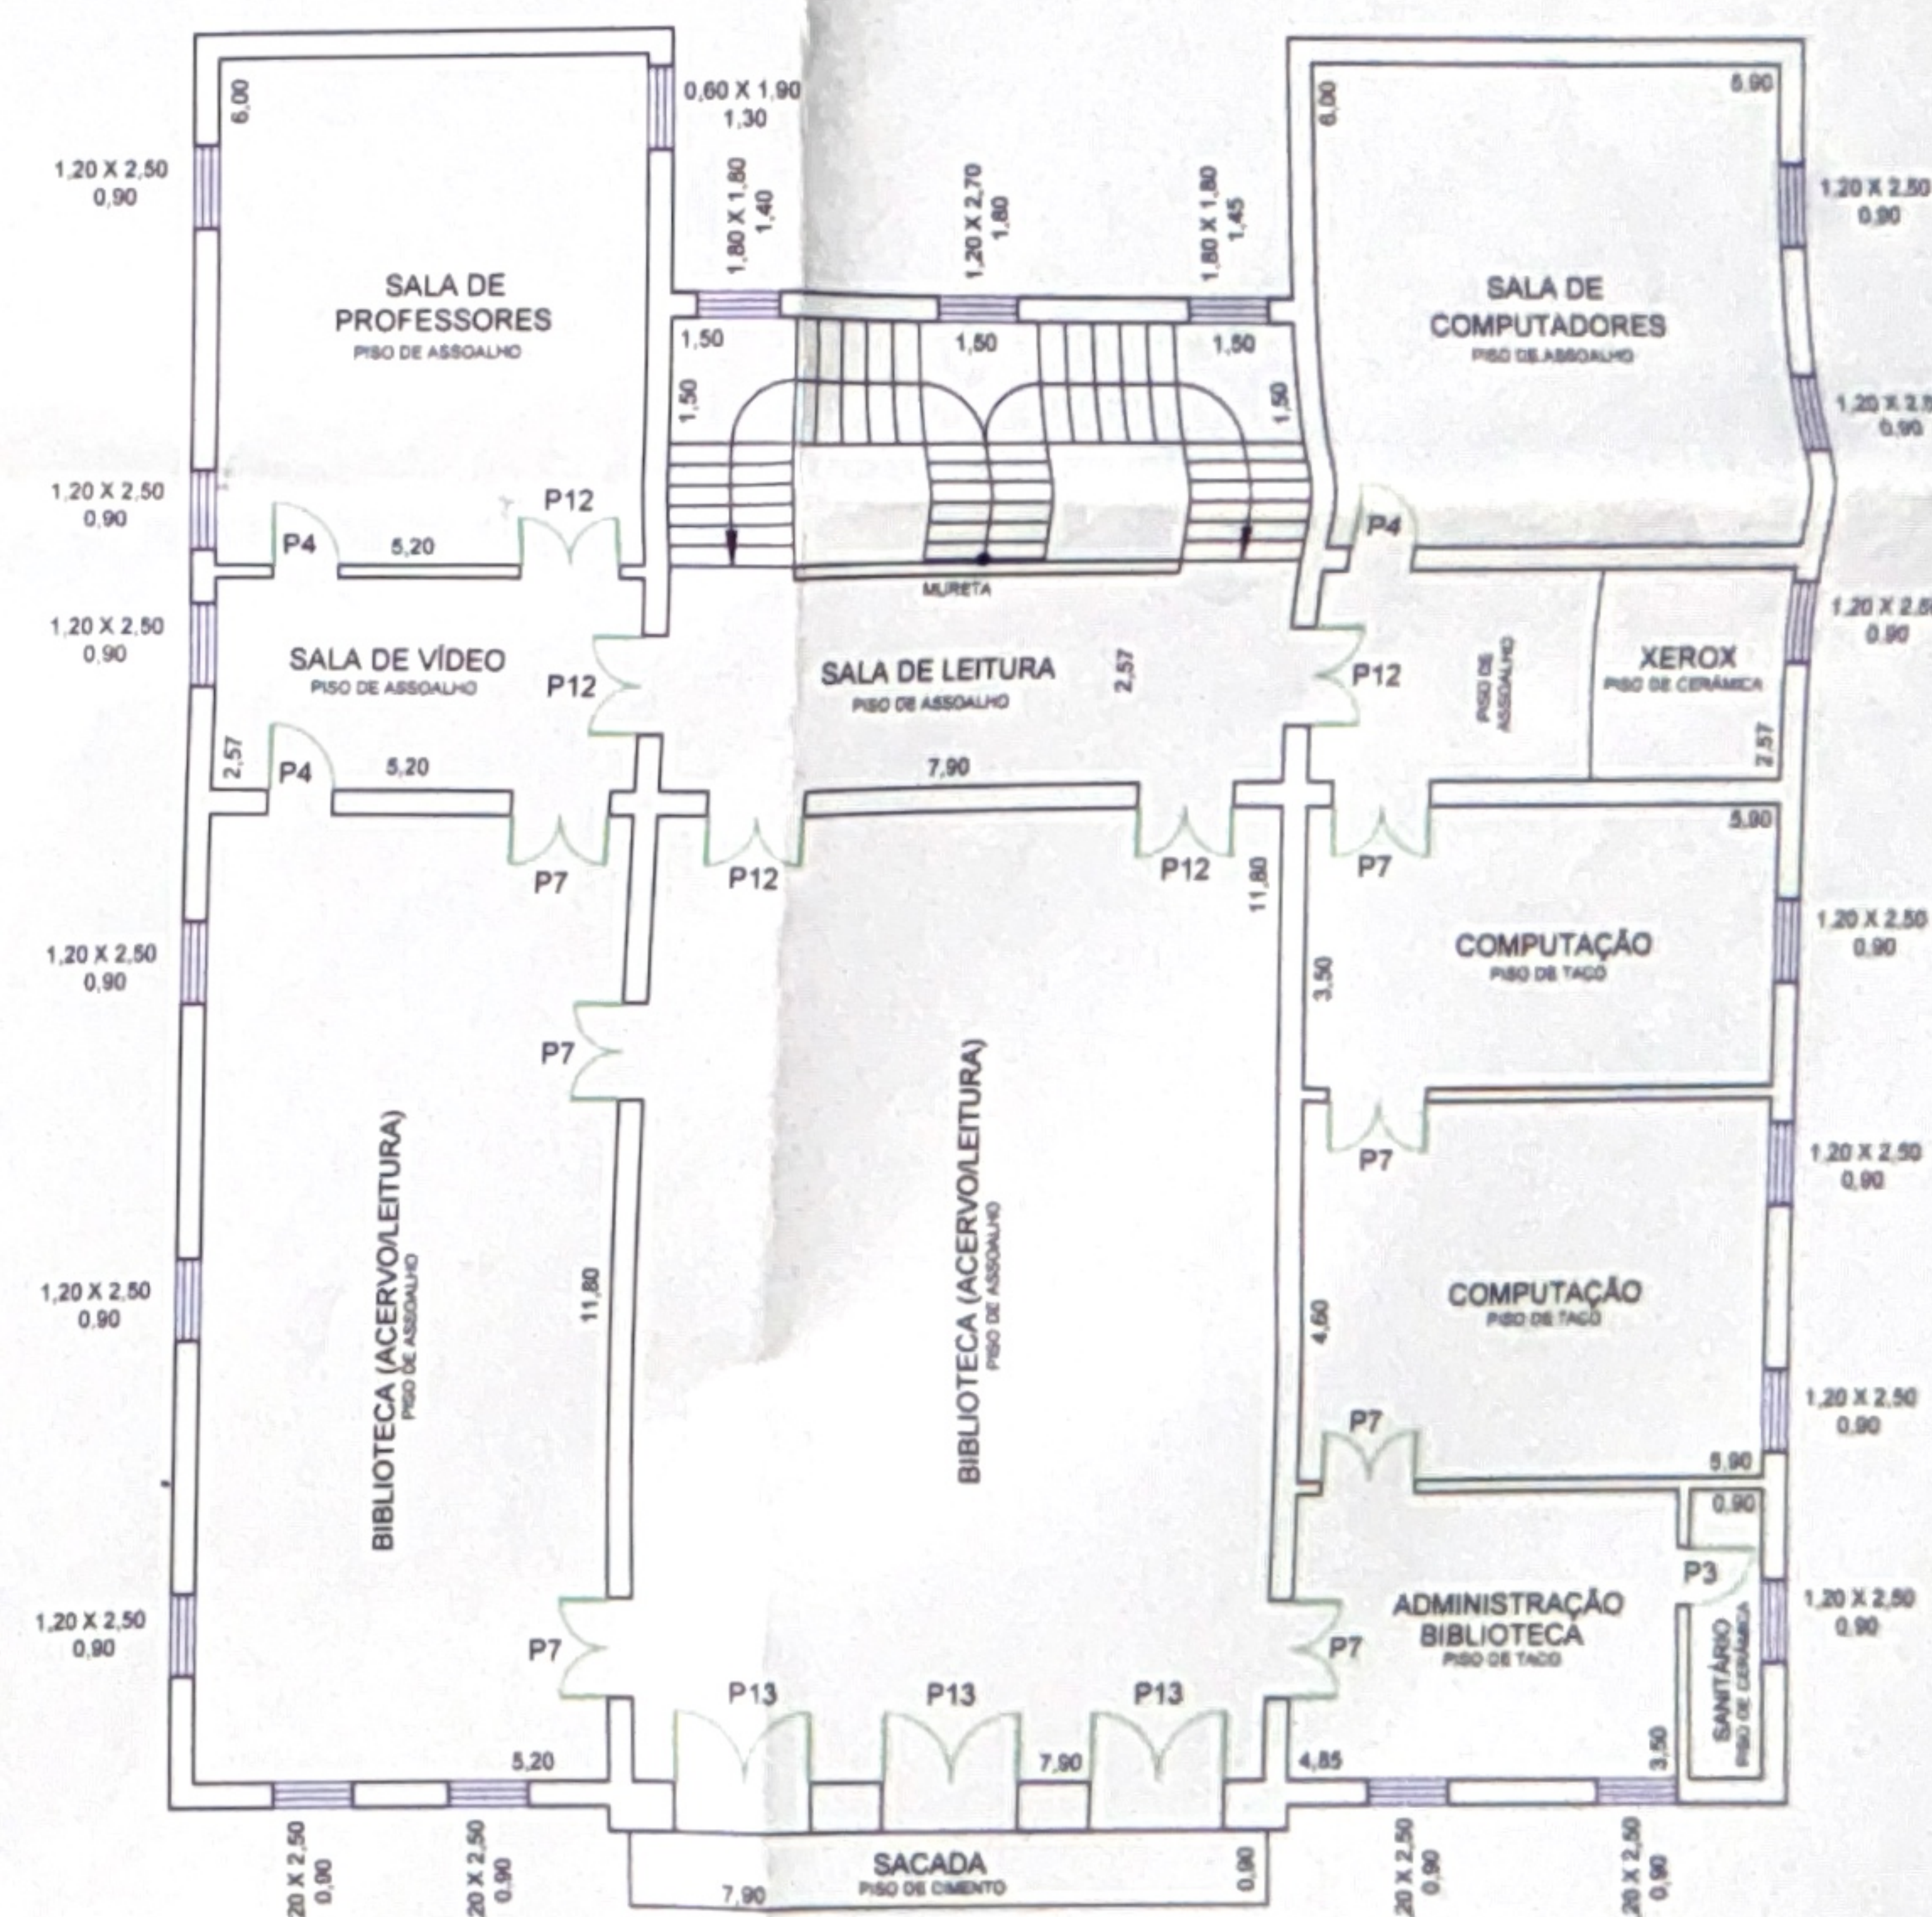

MEZANINO

ÁREA DO TERRENO 1.604,11 m²
 ÁREA DE OCUPAÇÃO 962,24 m²
 LIVRE 641,87 m²

PREFEITURA DO CAMPUS ADMINISTRATIVO DE SÃO CARLOS - USP		
PROJETO	ESCALA 1:100	SCPROJP
DESENHO LUÍS CARLOS BARBANO	DATA 23/07/2002	
TÍTULO	CENTRO DE DIVULGAÇÃO CIENTÍFICA E CULTURAL-CDCC	
(LOCALIZADO FORA DO CAMPUS)		ARQUITETURA
		FOLHA ÚNICA