





SUBSOLO

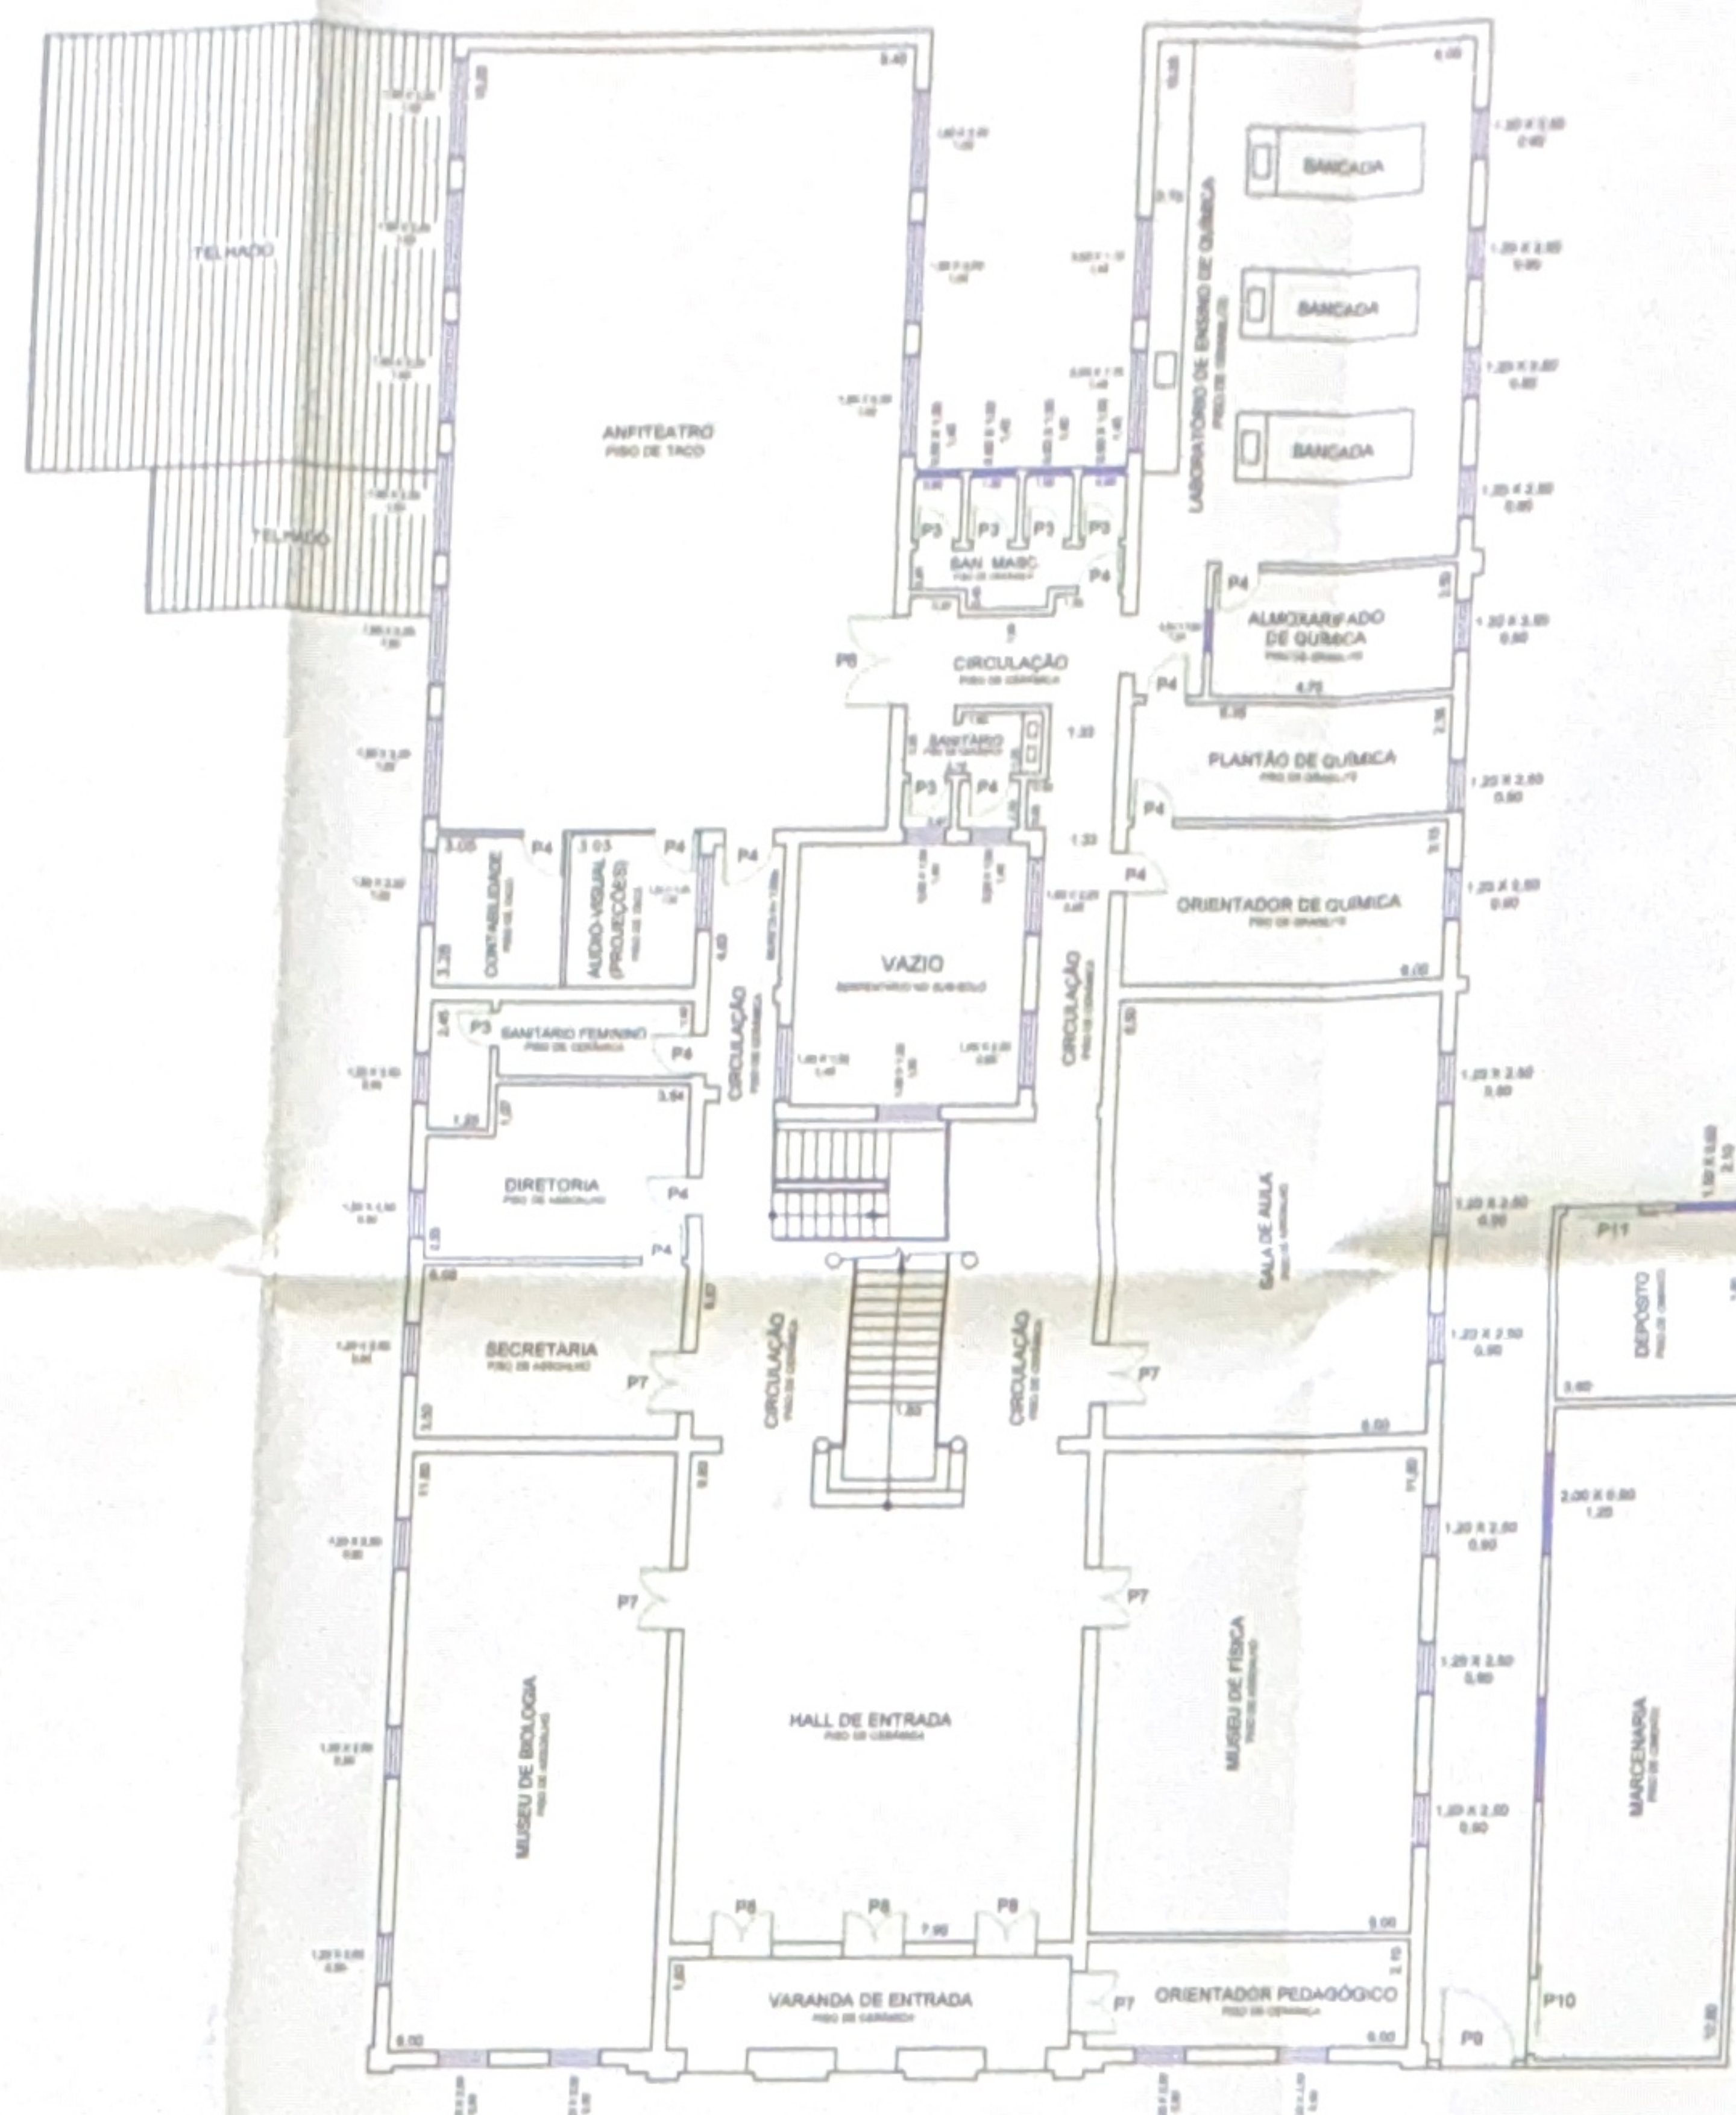

PAVIMENTO TÉRREO

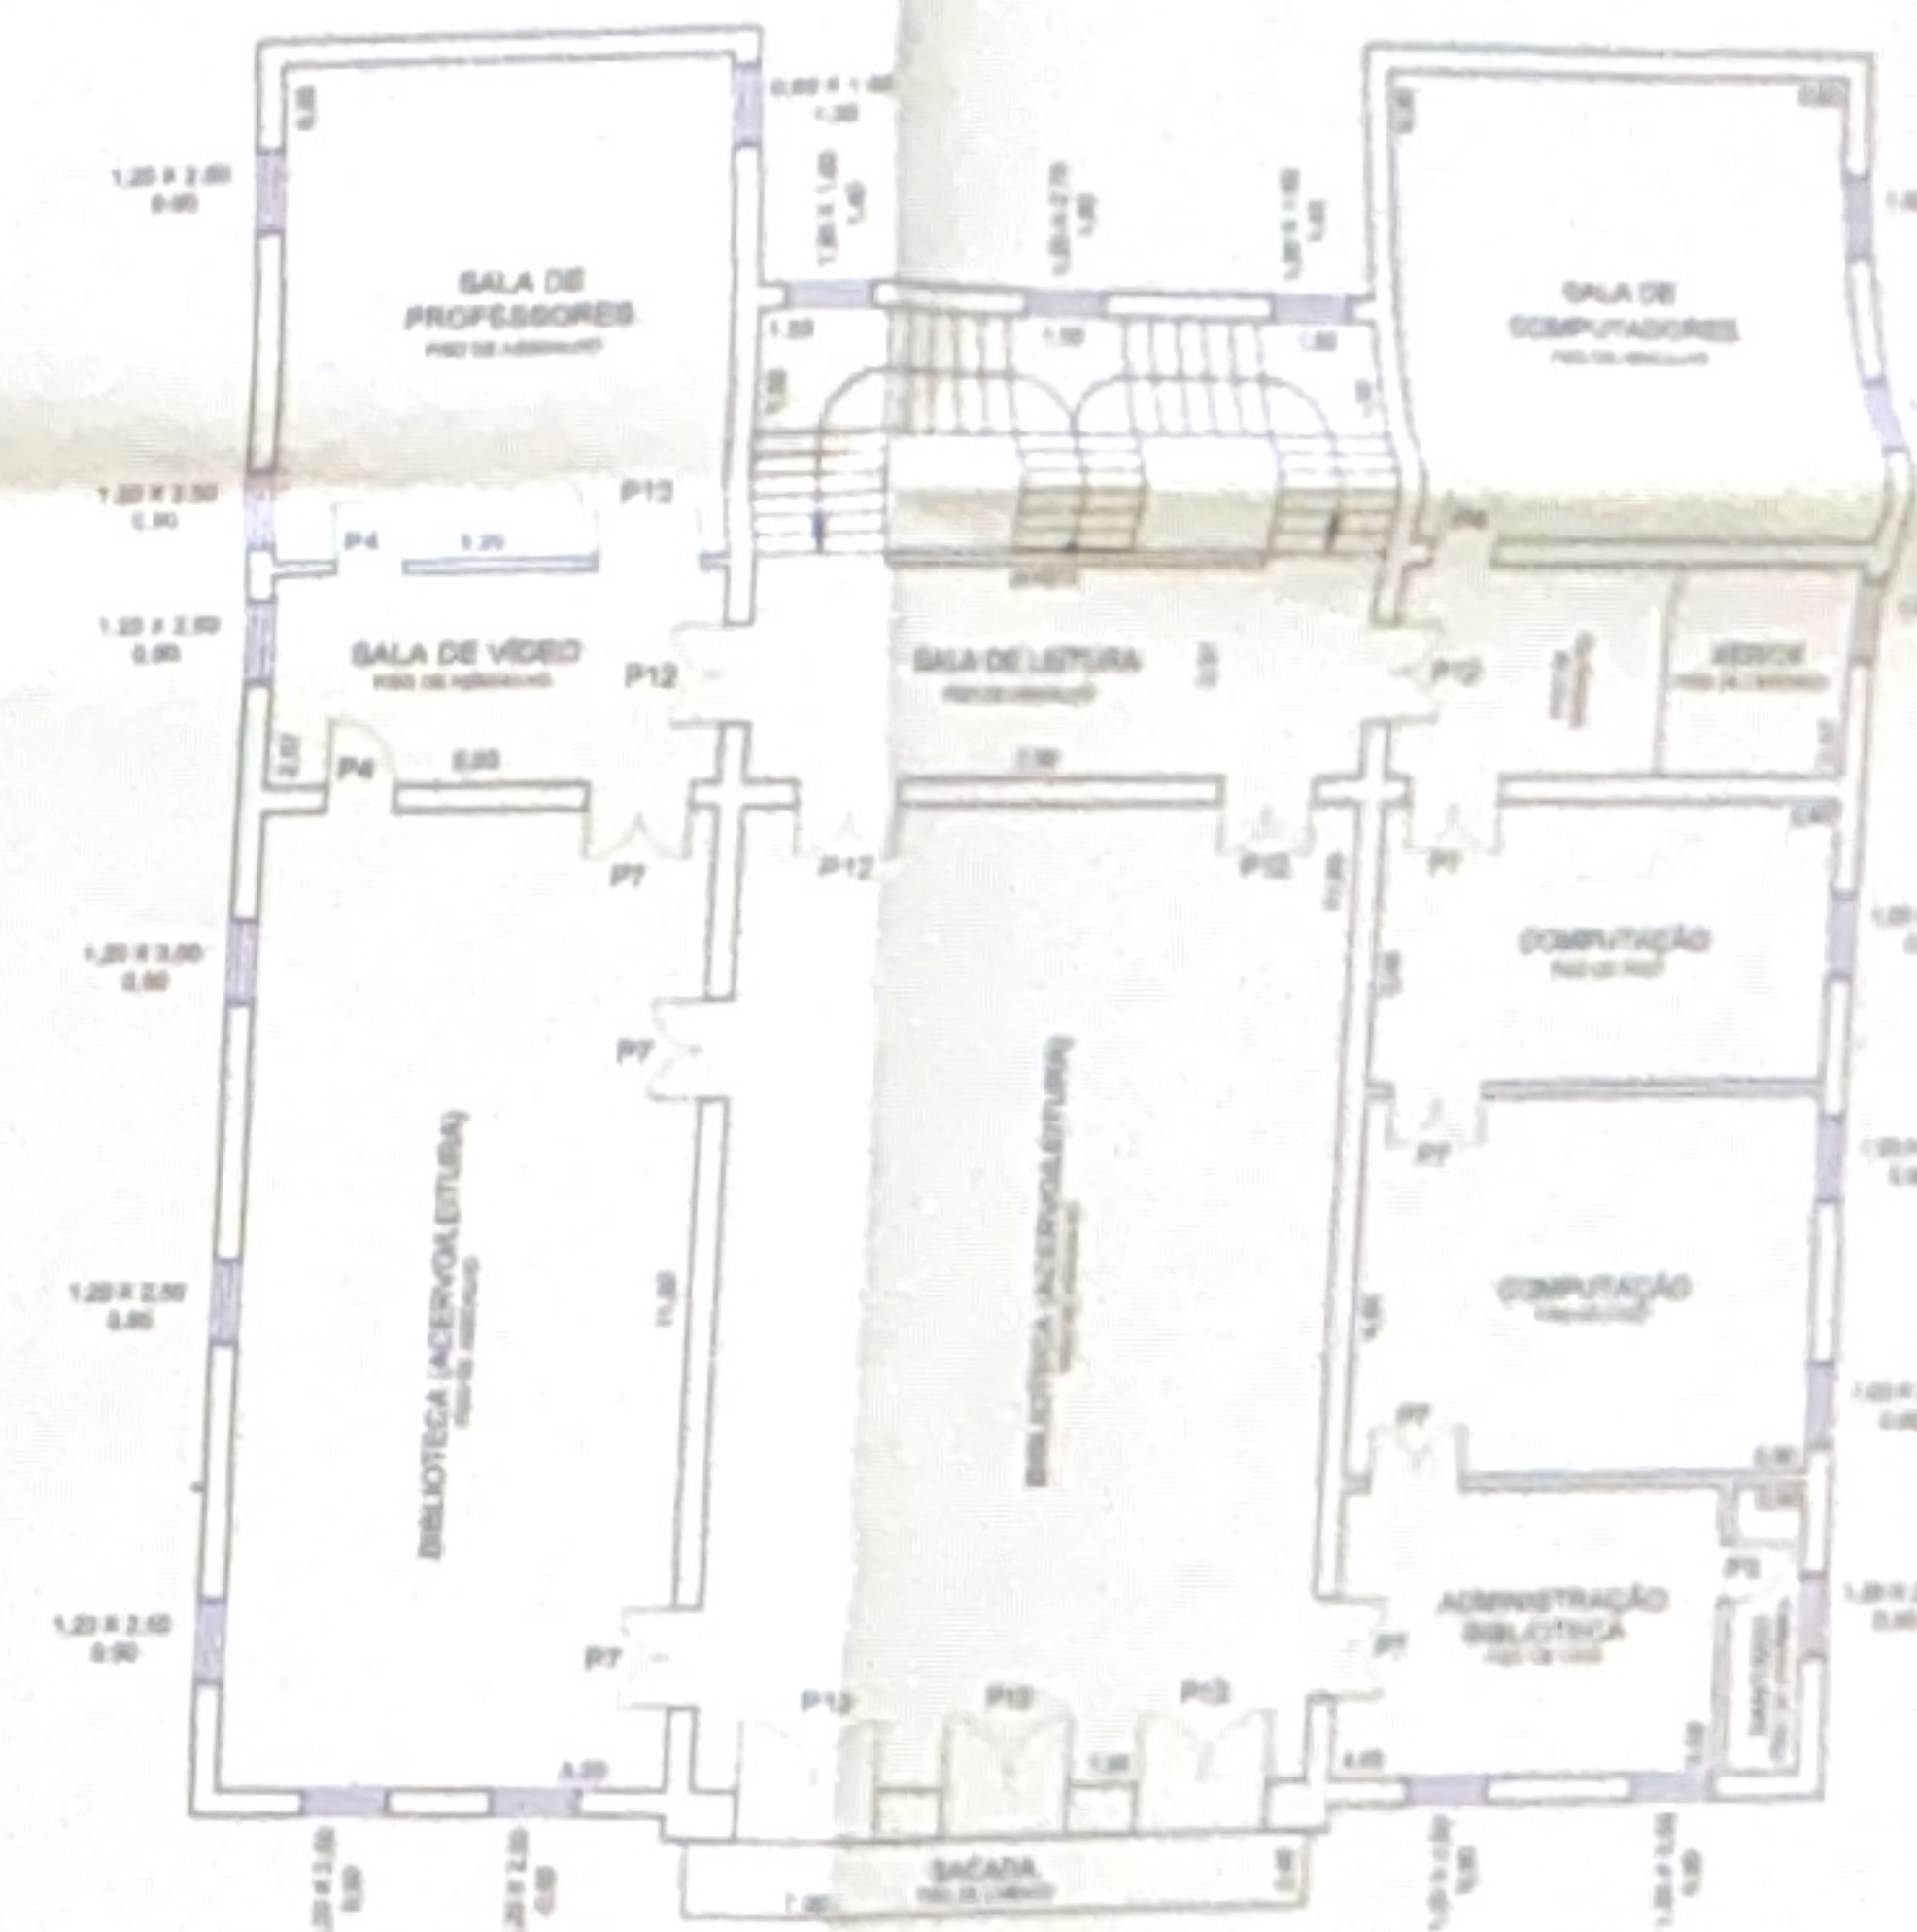

MEZANINO

TIPO	DIMENSÃO	MATERIAL	QUANT.
P1	0,80 x 2,10	ALUMÍNIO	06
P2	0,80 x 2,20	ALUMÍNIO	03
P3	0,75 x 2,10	ALUMÍNIO	10
P4	0,80 x 2,10	ALUMÍNIO	21
P5	1,00 x 1,80	ALUMÍNIO	07
P6	1,20 x 2,10	ALUMÍNIO	09
P7	1,20 x 2,10	ALUMÍNIO	12
P8	1,20 x 3,45	ALUMÍNIO	03
P9	1,40 x 1,90	ALUMÍNIO	01
P10	1,80 x 2,10	ALUMÍNIO	01
P11	1,40 x 1,90	ALUMÍNIO	04
P12	1,50 x 2,00	ALUMÍNIO	05
P13	1,70 x 2,00	ALUMÍNIO	03

ÁREA DO TERRENO..... 1.604,11 m²
 ÁREA DE OCUPAÇÃO..... 962,24 m²
 LIVRE..... 641,87 m²

PREFEITURA DO CAMPUS ADMINISTRATIVO DE SÃO CARLOS - USP		SCPROJP
PROJETO	ESCALA 1:100	
PROJETO	LUIZ CARLOS BARBOSA	DATA 23/07/2002
CENTRO DE DIVULGAÇÃO CIENTÍFICA E CULTURAL-CDCC		UNICA